TTABELA DE ALINHAMENTO HORIZONTAL - RAMO 900

Nº	DEFLEXÃO/ AZIMUTE	LC (m)	TT (m)	TL (m)	TC (m)	R (m)	D/L (m)	AC	TE-PC	ET-PT	PONTO	PI	TE-PC	ET-PT
C-902	-	-	15,654	-	-	71,000	30,816	024° 52' 03.92"	911+12,263	913+3,078	Y X	246439,9484 134762,5041	246436,3591 134747,2668	246449.6127 134774,8192
C-901	-	-	29,891	-	-	10,500	25,893	141° 17' 23.71"	910+6,370	911+12,263	Y X	246429,5054 134718,1719	246453,0488 134736,5891	246436.3591 134747,2668
C-900	-	-	11,985	-	-	91,000	23,834	015° 00' 22.21"	909+2,536	910+6,370	Y X	246462,4889 134743,9737	246469,6950 134753,5508	246453.0488 134736,5891

TABELA DE ALINHAMENTO HORIZONTAL - RAMO 950
TABELA DE ALINHAMENTO HORIZONTAL - L2E - DUPLICAÇÃO

Nº	DEFLEXÃO/ AZIMUTE	LC (m)	TT (m)	TL (m)	TC (m)	R (m)	D/L (m)	AC	TE-PC	ET-PT	PONTO	PI	TE-PC	ET-PT
C-950	-	-	11,813	-	-	91,000	23,494	014° 47' 33.07"	959+2,322	960+5,816	Y X	246400,2240 134710,1356	246393,2230 134700,6209	246409.4221 134717,5475
C-951	-	-	29,203	-	-	10,500	25,738	140° 26' 50.70"	960+5,816	961+11,555	Y X	246432,1612 134735,8706	246409,4221 134717,5475	246426.2964 134707,2628
C-952	-	-	15,983	-	-	71,000	31,442	025° 22' 21.92"	961+11,555	963+2,996	Y X	246423,0865 134691,6056	246426,2964 134707,2628	246413.4771 134678,8342
C-37	-	-	266,881	-	-	3008,400	532,368	010° 08' 20.70"	3071+10,658	3098+3,026	Y X	246417,0870 134758,0438	246597,5987 134954,6164	246273.9986 134532,7640
C-36	-	-	144,312	-	-	2950,000	288,394	005° 36' 04.56"	3057+2,265	3071+10,658	Y X	246695,2078 135060,9102	246781,9760 135176,2235	246597.5987 134954,6164

FAIXA DE ACELERAÇÃO - RAMO 900

Vel. Rodovia (km/h)	Vel. Conversão (km/h)	Rampa Média (i%)	Fator de Conversão	Faixa Acel./Desac. (m)	Compr. "Taper" (m)
80	20	+0,2	-	180,00	90

FAIXA DE DESACELERAÇÃO - RAMO 900

Vel. Rodovia (km/h)	Vel. Conversão (km/h)	Rampa Média (i%)	Fator de Conversão	Faixa Acel./Desac. (m)	Compr. "Taper" (m)
80	20	+0,6	-	125,00	90

FAIXA DE ACELERAÇÃO - RAMO 950

Vel. Rodovia (km/h)	Vel. Conversão (km/h)	Rampa Média (i%)	Fator de Conversão	Faixa Acel./Desac. (m)	Compr. "Taper" (m)
80	20	+0,8	-	180	90


FAIXA DE DESACELERAÇÃO - RAMO 950

Vel. Rodovia (km/h)	Vel. Conversão (km/h)	Rampa Média (i%)	Fator de Conversão	Faixa Acel./Desac. (m)	Compr. "Taper" (m)
80	20	-0,8	-	125,00	90

TABELA DE NARIZES FÍSICOS

ID	X (m)	Y (m)
NF24	134.722,4603	246.448,7095
NF25	134.746,1170	246.424,6153
NF26	134.707,7517	246.437,9506
NF27	134.731,7858	246.414,0476

PERFIL DUPLICAÇÃO SP-258

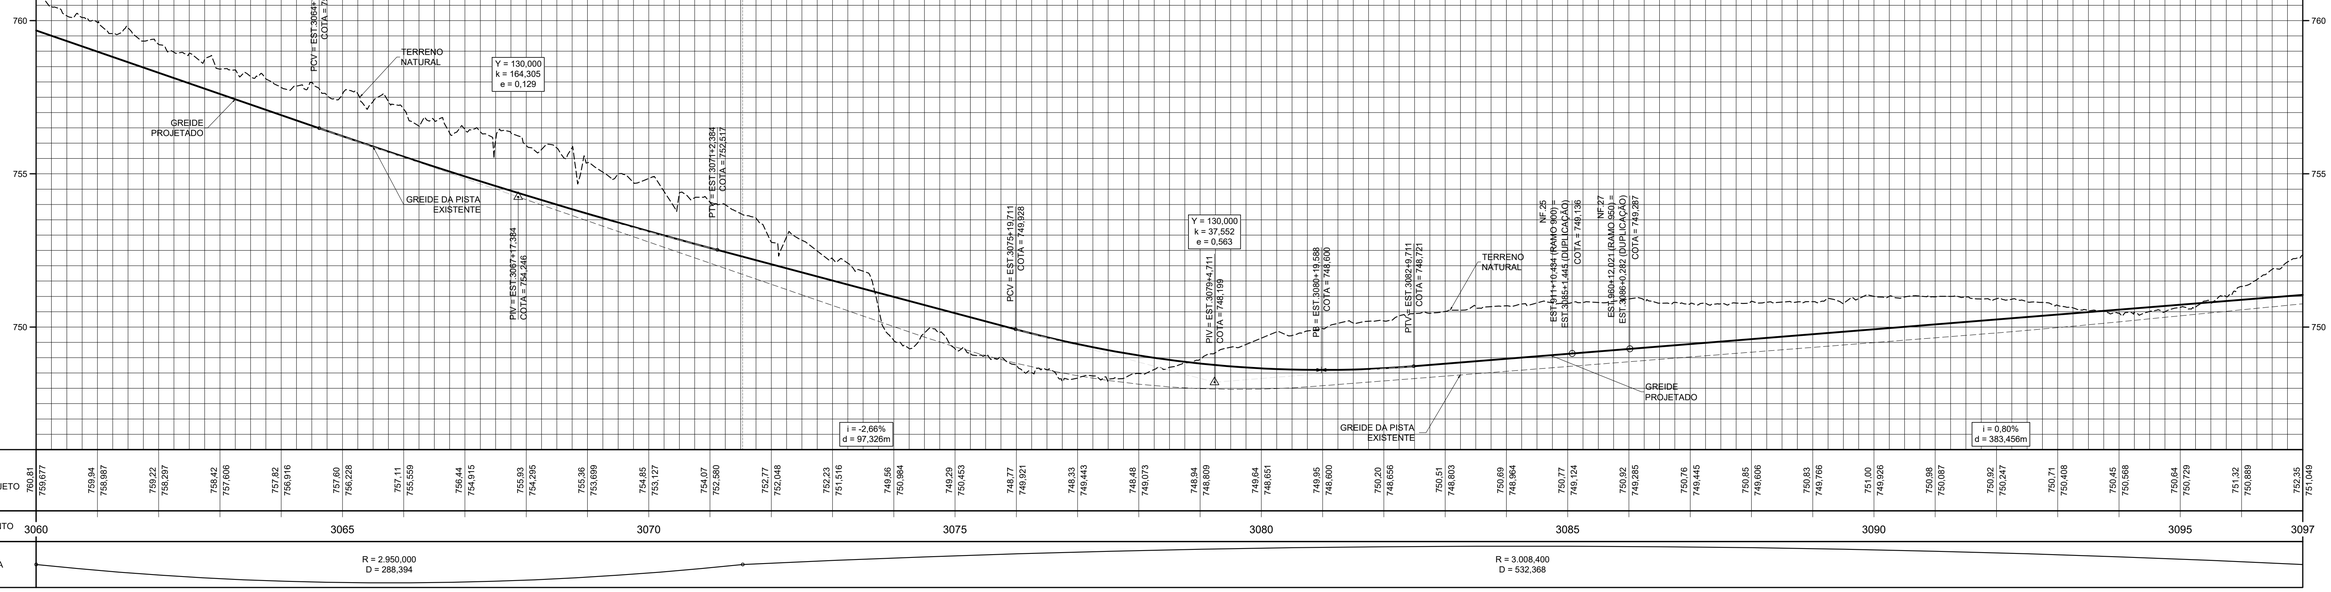

LEGENDA

- EIXOS DE PROJETO
- LIMITE DA PISTA (BORDOS DE PROJETO)
- ACOSTAMENTO PROJETADO
- PONTO BAIXO CANTEIRO CENTRAL
- PONTO ALTO DO GREIDE
- PONTO BAIXO DO GREIDE
- PISTA PROJETADA / FAIXA DE SEGURANÇA PROJETADA
- ACOSTAMENTO
- CANTEIROS
- PONTO DE ÔNIBUS
- PASSEIO PROJETADO
- O.A.E. PROJETADA
- O.A.E. EXISTENTE
- O.A.E. A DEMOLIR
- BARREIRA RÍGIDA DUPLA
- DIVISA DAS PROPRIEDADES (VER NOTA 04)
- FAIXA DE DOMÍNIO ESTIMADA (VER NOTA 04)
- FAIXA DE DOMÍNIO PROJETADA
- MURO DE CONTENÇÃO
- 699 / 700 / 701 CURVAS DE NÍVEL
- OFFSET DE CORTE
- OFFSET DE ATERRO
- SENTIDO TRÁFEGO

NOTAS:


1.MEDIDAS E COTAS EM METRO, EXCETO INDICAÇÃO CONTRÁRIA;
2.TALUDES UTILIZADOS NO PROJETO:
- CORTE H:V = 1:1
- CORTE H:V = 1,2:1
- ATERRO H:V = 1,5:1
- CANTEIROS H:V = VAR.:1;

3.SISTEMA DE COORDENADAS: PLANO TOPOGRAFICO LOCAL;
4.A INDICAÇÃO DE FAIXA DOMÍNIO EXISTENTE FOI ADOTADA COMO SENDO OS LIMITES DE MATRÍCULAS DOS TERRENOS LINDEIROS ADJACENTES À RODOVIA. NOS TRECHOS ONDE A MATRÍCULA NÃO FOI IDENTIFICADA, FOI TRAÇADA A POSIÇÃO DA FAIXA DE DOMÍNIO ESTIMADA;
5.PROJETO DE TOPOGRAFIA - VER DESENHO: DE-SP0000258-287.339-620-T01/101 A 109;
6.PROJETO DE INTERSEÇÃO - VER DESENHO: DE-SPD288258-288.289-620-F02/201 A 202.
7.HÁ LOCAIS ONDE A INCLINAÇÃO DO TALUDE NÃO SEGUE O PADRÃO 1:1,5 (ATERROS) E 1:1 (CORTES) DEVIDO A ANÁLISE DE ESTABILIDADE. PARA MAIS DETALHES - VER DESENHO: RT-SPD338258-338.339-620-G18/101.

SIGLAS - PLANTA PERFIL

PC = PONTO DE CURVA
PT = PONTO DE TANGÊNCIA
TE = TANGÊNCIA PARA ESPIRAL
EC = ESPIRAL PARA CIRCULAR
CE = CIRCULAR PARA ESPIRAL
ET = ESPIRAL PARA TANGÊNCIA
PI = PONTO DE INTERSEÇÃO
LC = COMPRIMENTO DA CURVA EM ESPIRAL
R = RAIO DA CURVA CIRCULAR
PCR = PONTO DE CURVATURA REVERSA
PCV = PONTO DE CURVATURA VERTICAL
PTV = PONTO DE TANGÊNCIA VERTICAL
PIV = PONTO DE INTERSEÇÃO VERTICAL
e = FLECHA OU ORDENADA MÁXIMA
Y = COMPRIMENTO DA PARÁBOLA
K = PARÂMETRO DA PARÁBOLA
PA = PONTO ALTO
PB = PONTO BAIXO

ARTICULAÇÃO DAS FOLHAS

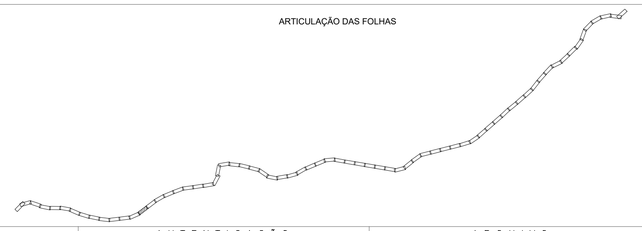

R0c	09/05/2023	Beatriz Mulinari CREA PR-22600/D		ATENDIMENTO A COMENTÁRIOS	
R0b	19/01/2023	Beatriz Mulinari CREA PR-22600/D		ATENDIMENTO A COMENTÁRIOS	
R0a	31/10/2022	Beatriz Mulinari CREA PR-22600/D		EMISSÃO INICIAL	
REV.	DATA	RESP. TÉC./PROJETISTA	RESP. TÉC./CONCES.	ASSUNTO	DOC. REFERÊNCIA

Intertechne

AUTENTICAÇÃO

ESTE DESENHO É ORIGINAL DE CÓPIA DE FLS _____
AUTOS Nº _____, APROVADO PELO
SR. DIRETOR DE ENGENHARIA ÀS FLS. _____ DOS AUTOS
Nº _____

CHEFE DA OBRA

ARQUIVO

Data	Prefixo	Número
Móvel	Gaveta	Divisão
Arquitetura		Mapa

ARTESP
AGÊNCIA DE TRANSPORTE DO ESTADO DE SÃO PAULO

VERIFICADO RESPONSÁVEL PELA ÁREA DE PROJETO

APROVADO RESPONSÁVEL TÉCNICO

CCR SPVias

Nº DESENHO INTERNO:	SV-SP258/00-0287.90-DUP-A1-GE/DE.E-157.R0c
Nº DESENHO ARTESP:	DE-SP0000258-287.339-620-F07/157
EMISSÃO	09/05/2023
TÍTULO:	PROJETO EXECUTIVO - PLANTA E PERFIL
RODOVIA:	SP-258- RODOVIA FRANCISCO ALVES NEGRÃO
TRECHO:	km 287+900 AO KM 338+110
ESTACA	EST. 3060+0,000 a 3097+0,000
ESCALA:	PLANTA 1:1000 PERFIL 1:100(V) - 1:1000(H)
FOLHA	157

DER SP

2217-SP-8-R0-G00-00-C-30-DE-0157