




RAMO DE SAÍDA DE 1 FAIXA

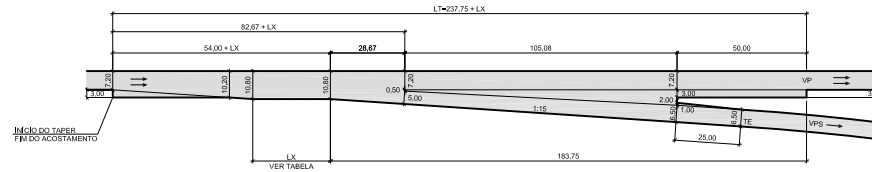


RAMO DE SAÍDA DE 1 FAIXA

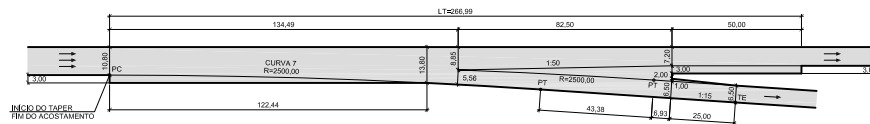

RAMO DE SAÍDA DE 2 FAIXAS

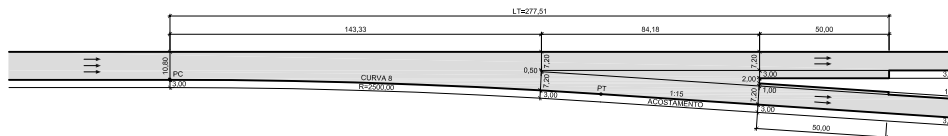

RAMO DE SAÍDA E RAMO SUCESSIVO DE ENTRADA

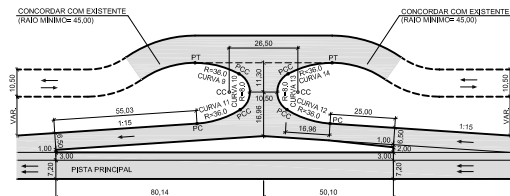

PROJETO PADRÃO DE RAMOS DE SAÍDA

TIPO	RAMO DE SAÍDA COM	COMPROMISSO TOTAL DA FAIXA DE DESACELERAÇÃO (m)	OBSERVAÇÃO
1	1 FAIXA	237,75 + Lx	SEM REDUÇÃO DE FAIXA NA VIA PRINCIPAL
2	1 FAIXA	266,09	COM REDUÇÃO DE 1 FAIXA NA VIA PRINCIPAL
3	2 FAIXA	277,51	COM REDUÇÃO DE 1 FAIXA NA VIA PRINCIPAL
4	1 FAIXA	-	COM RAMO SUCESSIVO DE ENTRADA

ELEMENTOS DE CURVA

CURVA N°	RAIO (m)	ANGULO CENTRAL (m)	TANGENTE (T) (m)	DESENVOLVIMENTO (D) (m)
7	2500,00	3°48'50,84"	83,24	166,42
8	2500,00	3°48'50,87"	83,24	166,42
9 + 14	36.000	28°53'00,00"	6.000	17.655
10 + 13	6.000	119°58'26,20"	13.849	16.752
11 + 12	36.000	28°50'50,13"	6.014	17.664

TABELA DE VALORES DE "LX" PARA NARIZ TIPO 1

VP (km/h)	VPS (km/h)							
	0	20	30	40	50	60	70	80
50	LX0,00	LX0,00	LX0,00	-	-	-	-	-
60	LX0,00	LX0,00	LX0,00	LX0,00	-	-	-	-
70	LX0,00	LX0,00	LX0,00	LX0,00	LX0,00	-	-	-
80	LX0,00	LX0,00	LX0,00	LX0,00	LX0,00	LX0,00	-	-
90	LX0,00	LX0,00	LX0,00	LX0,00	LX0,00	LX0,00	LX0,00	-
100	LX0,00	LX0,00	LX0,00	LX0,00	LX0,00	LX0,00	LX0,00	LX0,00
110	LX0,00	LX0,00	LX0,00	LX0,00	LX0,00	LX0,00	LX0,00	LX0,00
120	LX=18,25	LX=11,25	LX=2,25	LX0,00	LX0,00	LX0,00	LX0,00	LX0,00

LEGENDA:

VP = VELOCIDADE DE PROJETO NA PISTA,
VPS = VELOCIDADE DE PROJETO NO RAMO

NOTAS:

- 1 - MEDIDAS EM METRO, EXCETO INDICAÇÃO EM CONTRÁRIO.
- 2 - UTILIZAR A FAIXA DE TRAFEGO DE 3,00m PARA IMPLANTAÇÃO DE PISTAS NOVAS. EXCEPCIONALMENTE, PODERÁ SER ADOPTADA A LARGURA DE 3,50m PARA AMPLIAÇÃO DE PISTAS EXISTENTES.
- 3 - PARA GREIDES ASCENDENTES MAIORES QUE 2%, VERIFICAR A NECESSIDADE DE INTRODUZIR UMA FAIXA AUXILIAR PARALELA DE EXTENSÃO SUFICIENTE, PARA GARANTIR A ENTRADA SEGURA DE CAMINHÕES NA FAIXA DE TRAFEGO DA PISTA.
- 4 - OS ESTUDOS DE TRAFEGO DEVERÃO DEFINIR O TIPO DE NÁVEIS A SER ADOPTADO.

												ESTA FOLHA E PROPRIEDADE DO DER-DEPARTAMENTO DE ESTRADAS DE RODAGEM DO ESTADO DE SÃO PAULO E SEU CORRELADO. NÃO PODE SER COPIADA OU REPRODUZIDA A TERCEIROS. A LIBERAÇÃO OU A APROVAÇÃO DESTA DOCUMENTAÇÃO NÃO ENTRA A DETALHISTA DE SUA RESPONSABILIDADE SOBRE O USUÁRIO.		DER Departamento de Estradas de Rodagem do Estado de São Paulo	
										EMPREENDIMENTO:		TRECHO:			
										OBJETO: PROJETO PADRÃO DE GEOMETRIA					
										RAMOS DE SAÍDA DE 1 e 2 FAIXAS - TIPOS 1, 2, 3 e 4					
										VERIFICAÇÃO		APROVAÇÃO			
										ELAB. MAURO MORAES		RAMOS DE SAÍDA DE 1 e 2 FAIXAS - TIPOS 1, 2, 3 e 4			
										DES. MAURO GONÇALVES		ESCALA: 1:1000			
										CHEFE. ENR. CARLOS C. LUSTOSA		CÓDIGO: PP-DE-F07/014			
										RESP.TEC. ENR. EDUARDO KOBACH JUN.		REVISÃO: A			